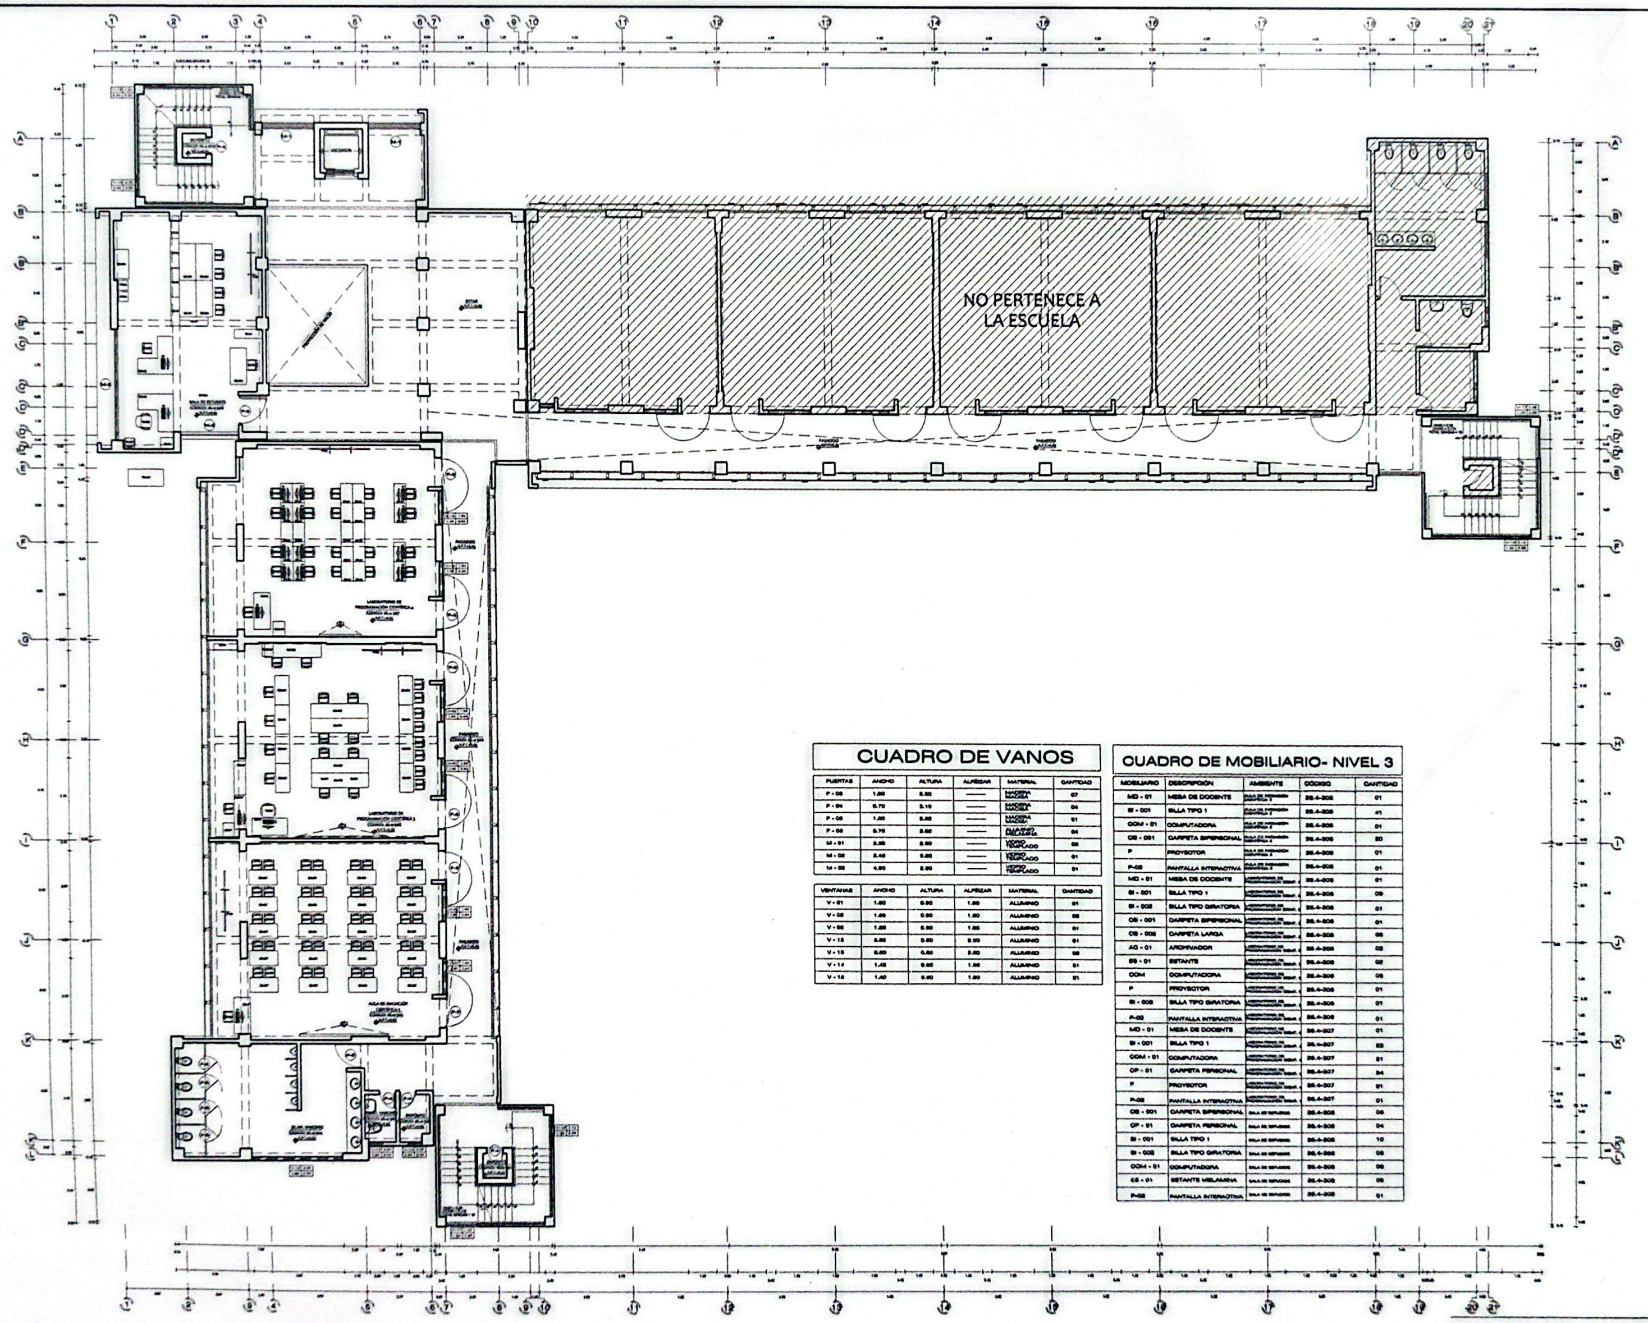


CUADRO DE VANOS

PUERTAS	ANCHO	ALTURA	ALFÉIZAR	MATERIAL	CANTIDAD
P - 06	1.00	2.10	———	MADERA MACIZA	07
P - 04	0.70	2.10	———	MADERA MACIZA	04
P - 05	1.00	2.10	———	MADERA MACIZA	01
P - 08	0.70	2.10	———	CONTRAPLACADO MELAMINA	04
M - 01	2.25	2.10	———	VIDRIO TEMPLADO	08
M - 02	2.40	2.10	———	VIDRIO TEMPLADO	01
M - 03	4.00	2.10	———	VIDRIO TEMPLADO	01

VENTANAS	ANCHO	ALTURA	ALFÉIZAR	MATERIAL	CANTIDAD
V - 01	1.80	0.90	1.00	ALUMINIO	01
V - 02	1.40	0.90	1.00	ALUMINIO	09
V - 06	1.80	0.90	1.00	ALUMINIO	01
V - 13	5.85	0.90	0.90	ALUMINIO	01
V - 15	6.60	0.90	2.80	ALUMINIO	02
V - 14	1.45	0.90	1.00	ALUMINIO	01
V - 16	1.40	0.90	1.00	ALUMINIO	01

CUADRO DE MOBILIARIO- NIVEL 3

MOBILIARIO	DESCRIPCIÓN	AMBIENTE	CODIGO	CANTIDAD
MD - 01	MESA DE DOCENTE	AULA DE CAPACITACIÓN	DS.A-305	01
SI - 001	SILLA TIPO 1	AULA DE CAPACITACIÓN	DS.A-305	41
COM - 01	COMPUTADORA	AULA DE CAPACITACIÓN	DS.A-305	01
CR - 001	CARPETA SIPERSONAL	AULA DE CAPACITACIÓN	DS.A-305	80
P	PROYECTOR	AULA DE CAPACITACIÓN	DS.A-305	01
P-05	PANTALLA INTERACTIVA	AULA DE CAPACITACIÓN	DS.A-305	01
MD - 01	MESA DE DOCENTE	LABORATORIO DE PROGRAMACIÓN	DS.A-305	01
SI - 001	SILLA TIPO 1	LABORATORIO DE PROGRAMACIÓN	DS.A-305	09
SI - 002	SILLA TIPO GIRATORIA	LABORATORIO DE PROGRAMACIÓN	DS.A-305	01
CR - 001	CARPETA SIPERSONAL	LABORATORIO DE PROGRAMACIÓN	DS.A-305	01
CR - 002	CARPETA LARGA	LABORATORIO DE PROGRAMACIÓN	DS.A-305	09
AC - 01	ARCHIVADOR	LABORATORIO DE PROGRAMACIÓN	DS.A-305	02
ES - 01	ESTANTE	LABORATORIO DE PROGRAMACIÓN	DS.A-305	02
COM	COMPUTADORA	LABORATORIO DE PROGRAMACIÓN	DS.A-305	09
P	PROYECTOR	LABORATORIO DE PROGRAMACIÓN	DS.A-305	01
SI - 002	SILLA TIPO GIRATORIA	LABORATORIO DE PROGRAMACIÓN	DS.A-305	01
P-02	PANTALLA INTERACTIVA	LABORATORIO DE PROGRAMACIÓN	DS.A-305	01
MD - 01	MESA DE DOCENTE	AULA DE CAPACITACIÓN	DS.A-307	01
SI - 001	SILLA TIPO 1	AULA DE CAPACITACIÓN	DS.A-307	52
COM - 01	COMPUTADORA	AULA DE CAPACITACIÓN	DS.A-307	01
CP - 01	CARPETA PERSONAL	AULA DE CAPACITACIÓN	DS.A-307	54
P	PROYECTOR	AULA DE CAPACITACIÓN	DS.A-307	01
P-05	PANTALLA INTERACTIVA	AULA DE CAPACITACIÓN	DS.A-307	01
CS - 001	CARPETA SIPERSONAL	SALA DE DOCENTES	DS.A-308	06
CP - 01	CARPETA PERSONAL	SALA DE DOCENTES	DS.A-308	04
SI - 001	SILLA TIPO 1	SALA DE DOCENTES	DS.A-308	10
SI - 002	SILLA TIPO GIRATORIA	SALA DE DOCENTES	DS.A-308	06
COM - 01	COMPUTADORA	SALA DE DOCENTES	DS.A-308	06
ES - 01	ESTANTE MELAMINA	SALA DE DOCENTES	DS.A-308	06
P-05	PANTALLA INTERACTIVA	SALA DE DOCENTES	DS.A-308	01

TERCER NIVEL
ESC: 1/150

ÁREA FUERA DE ACREDITACIÓN

ARQUITECTURA
PLANO DE DISTRIBUCIÓN

Proyecto: ACTUALIZACIÓN DE PLANOS ESCUELA P. DE CIENCIAS DE LA COMPUTACIÓN

Observaciones:

Propietario: UNIVERSIDAD NACIONAL DE SAN AGUSTÍN

Revisado por: ETGRD

Aprobado por: AYCH

Dibujado por: FAVS

Elaborado por:
UNIDAD DE RESPONSABILIDAD SOCIAL
EQUIPO TÉCNICO ESPECIALIZADO EN: GESTIÓN DE RIESGOS DE DESASTRES

Dirección: AV. VENEZUELA S/N


Distrito: Arequipa
Provincia: Arequipa
Departamento: Arequipa

Escala: INDICADA

Fecha: 18 MARZO 2026

ID de Plano:

A-04

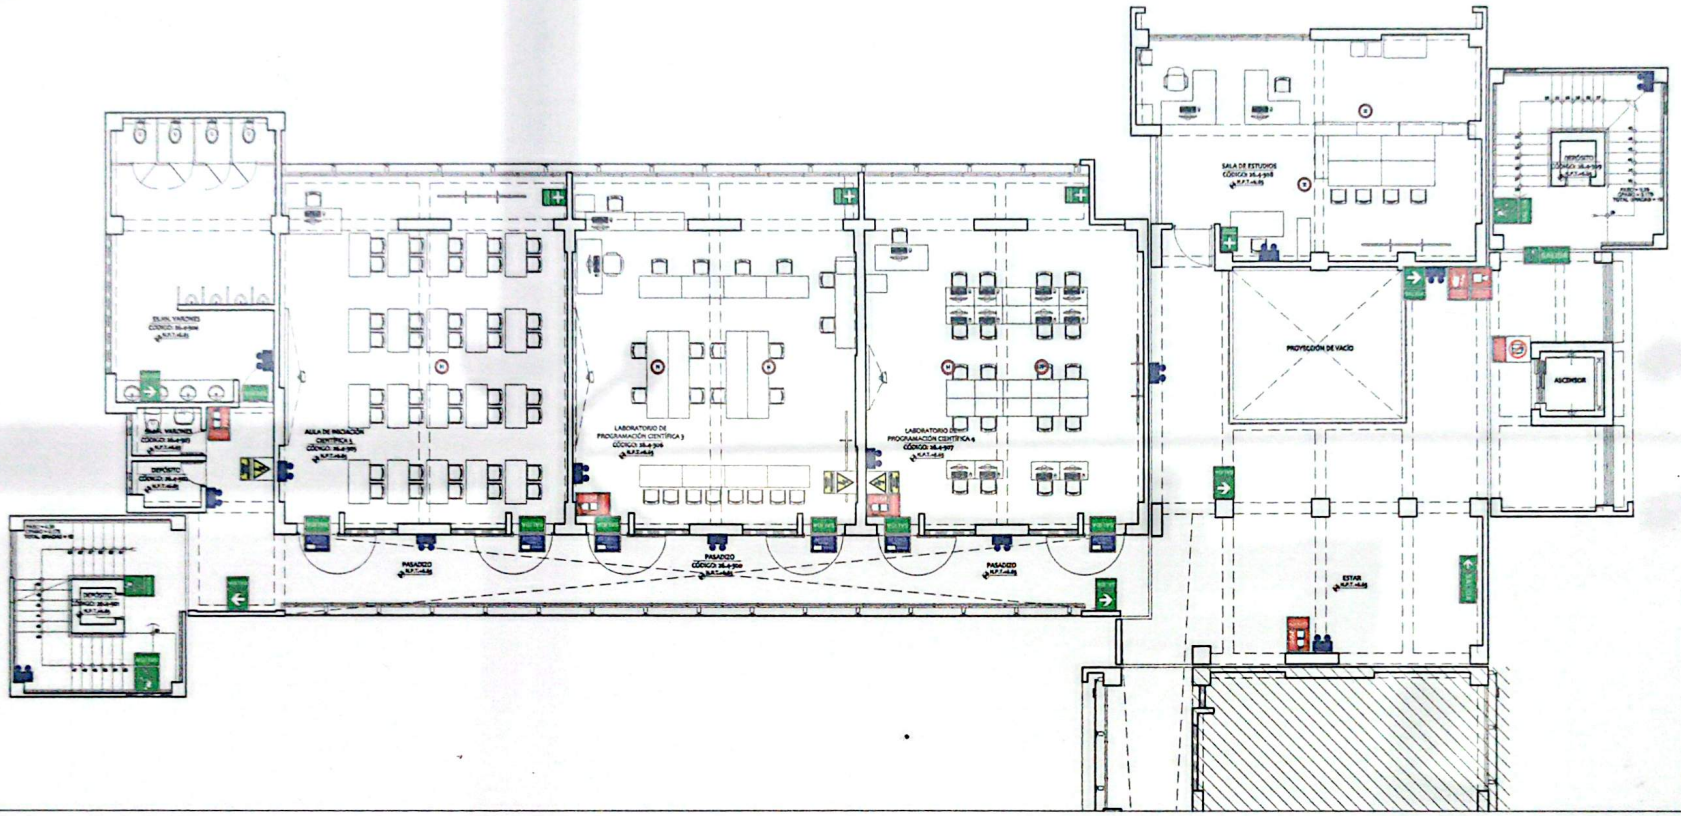

LEYENDA

SALIDA	RUTA DE EVACUACIÓN: SALIDA	SALIDA / SALIDA	CARTEL COLGANTE: -BAJAR POR ESCALERA A LA IZQUIERDA -BAJAR POR ESCALERA A LA DERECHA		PULSADOR DE ALARMA EN PARED CON SIRENA Y LUZ ESTROMBOTICA	H	DETECTOR DE HUMO
SALIDA	RUTA DE EVACUACIÓN: SALIDA A LA DERECHA	SALIDA / SALIDA	CARTEL COLGANTE: -SALIDA A LA IZQUIERDA -SALIDA A LA DERECHA		EXTINTOR CONTRA INCENDIO (tipo extintor, capacidad, clase fuego)		LUZ DE EMERGENCIA
SALIDA	RUTA DE EVACUACIÓN: SALIDA A LA IZQUIERDA		PRIMEROS AUXILIOS		AVISADOR SONORO EN CASO DE INCENDIO	AFORO	CARTEL DE CAPACIDAD MÁXIMA DEL ESTABLECIMIENTO
SALIDA SALIDA	RUTA DE EVACUACIÓN: BAJAR POR ESCALERA		ADVERTENCIA POR RIESGO ELÉCTRICO		ASCENSOR: NO USAR EN CASO DE SISMO O INCENDIO		

TERCER NIVEL

ESC: 1/100

PERTENECE A OTRA ESCUELA PROFESIONAL

ARQUITECTURA

PLANO DE SEÑALIZACIÓN

Proyecto: ACTUALIZACIÓN DE PLANOS ESCUELA P. DE CIENCIAS DE LA COMPUTACIÓN

Observaciones:

Propietario: UNIVERSIDAD NACIONAL DE SAN AGUSTÍN

Revisado por: ETGAD

Aprobado por: AFCHF

Validador DAO: JRAC

Elaborado por: UNIDAD DE RESPONSABILIDAD SOCIAL

EQUIPO TÉCNICO ESPECIALIZADO EN GESTIÓN DE RIESGOS DE DESASTRES

Dirección: AV. VENEZUELA S/N

Distrito: Arequipa
Provincia: Arequipa
Departamento: Arequipa

Escala: INDICADA

Fecha: 29 ABRIL 2026

ID de Plano: